


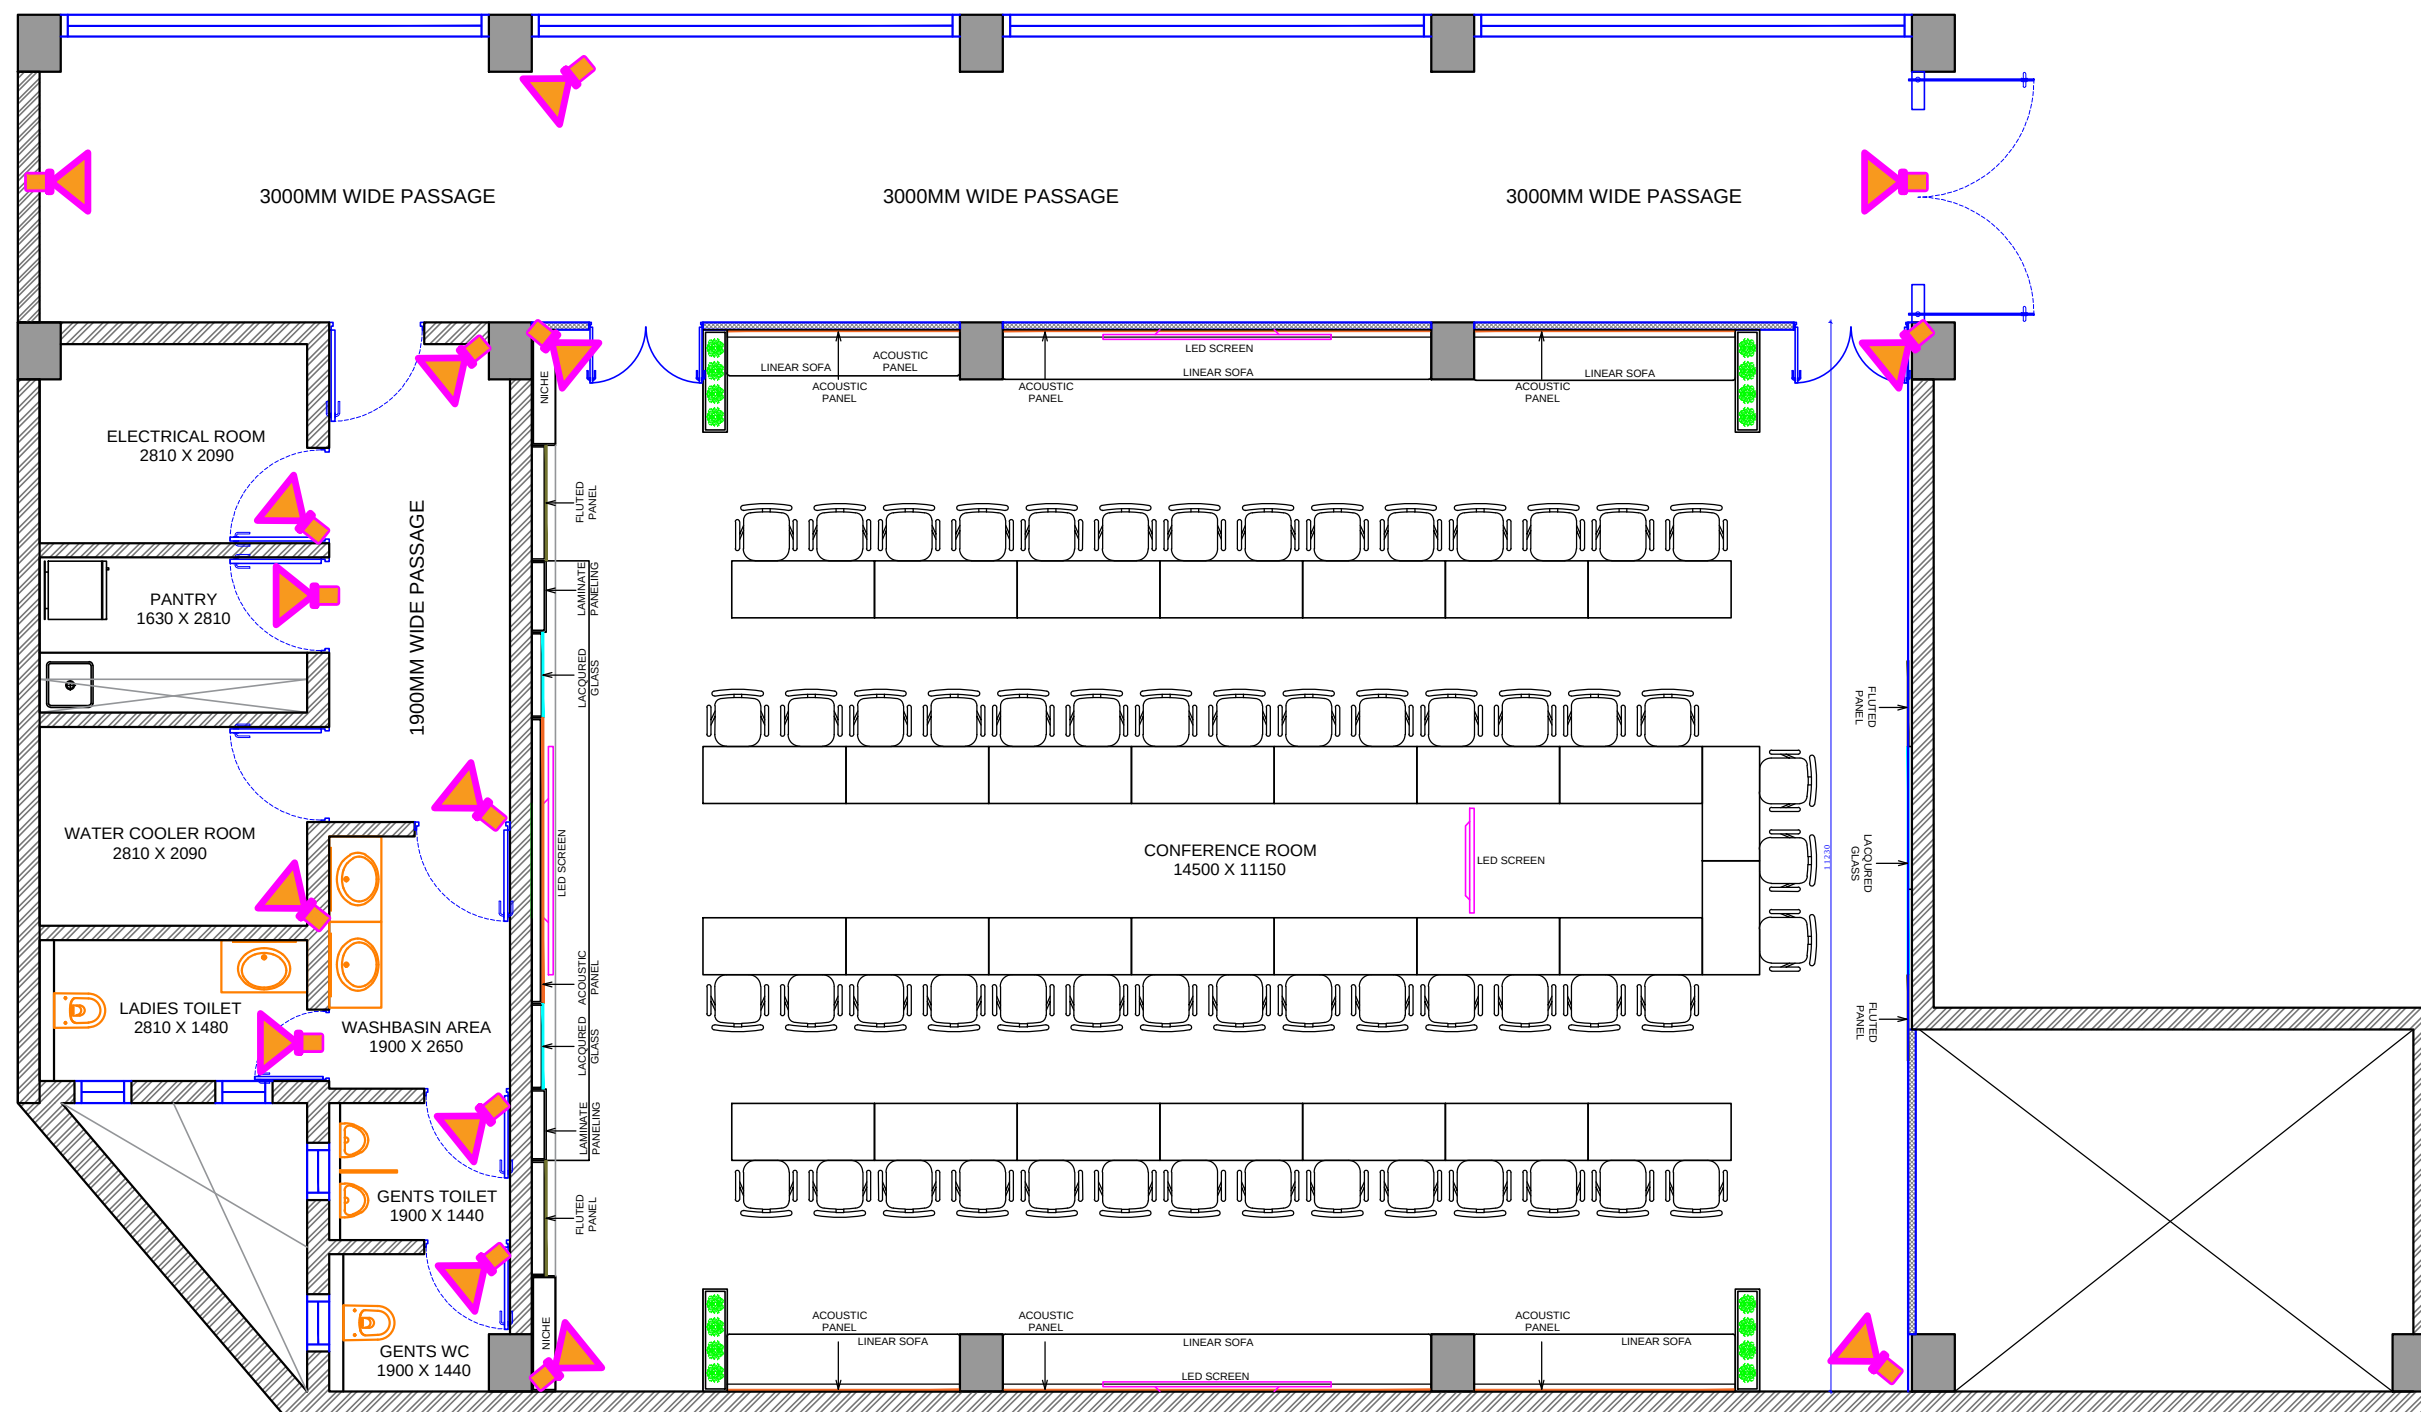

INTERIOR LAYOUT  
CONFERENCE ROOM

GENERAL NOTES :

1. All dimensions are in MM.
2. Written dimensions are to be followed. The drawing is not to be scaled.
3. Any discrepancy in the drawing should be brought to the notice of the architects immediately, and prior to commencing any work from this drawing.
4. Any addition or alteration to this drawing should not be made without the written consent of the architects.
5. All work shall be executed in accordance with the best practices to relevant Indian standard codes of practice.
6. Construction from these drawing is subject to all statutory approvals.
7. This drawing must be read in conjunction with other architectural, structural, interior, landscape and utility drawings.
8. Indicated all levels are finished.
9. Contractor & engineer shall check & verify all dimensions & M before execution of the work. & bring to the notice of the architect any discrepancy.

CLIENT :



FIRE CONSULTANT:

ELECTRICAL CONSULTANT:

HVAC CONSULTANT:

CHECKED

APPROVED

GFC-DWG

DATE:

SIGNATURE

PURPOSE

R.NO

DESCRIPTION

DATE

PROJECT :

Gujarat Industrial Development Corporation  
First Floor, Block 5, Udhog Bhavan, Sector-11,  
Gandhinagar 382 011, Gujarat, India.

TITLE :

INTERIOR LAYOUT  
CONFERENCE ROOM

PID-AHD-KE-GI-64

DWG NO: INT-01

REV:

SCALE: N.T.S

DRAWN BY: KEVAL

R0

DATE: 18-02-2026

CHECKED BY: SP



**Sthapati Architecture &  
Interiors Pvt.Ltd.**

www.ssthaipg.com  
302, Silver Radiance, Sindhubhavan Marg,  
Pakwan, Bodakdev,  
Ahmedabad-380054. Phone: +91 79 26871665.  
Email ID: sureshstha@sthatipatigroup.com

Contractors, vendors & consultants must verify all dimension on site and notify this Company any discrepancies prior to carry out work. Written dimensions take precedence over scaled dimensions. Sthapati Architecture & Interiors Pvt.Ltd. retains copyright on this drawing.

GFC DRG.

